


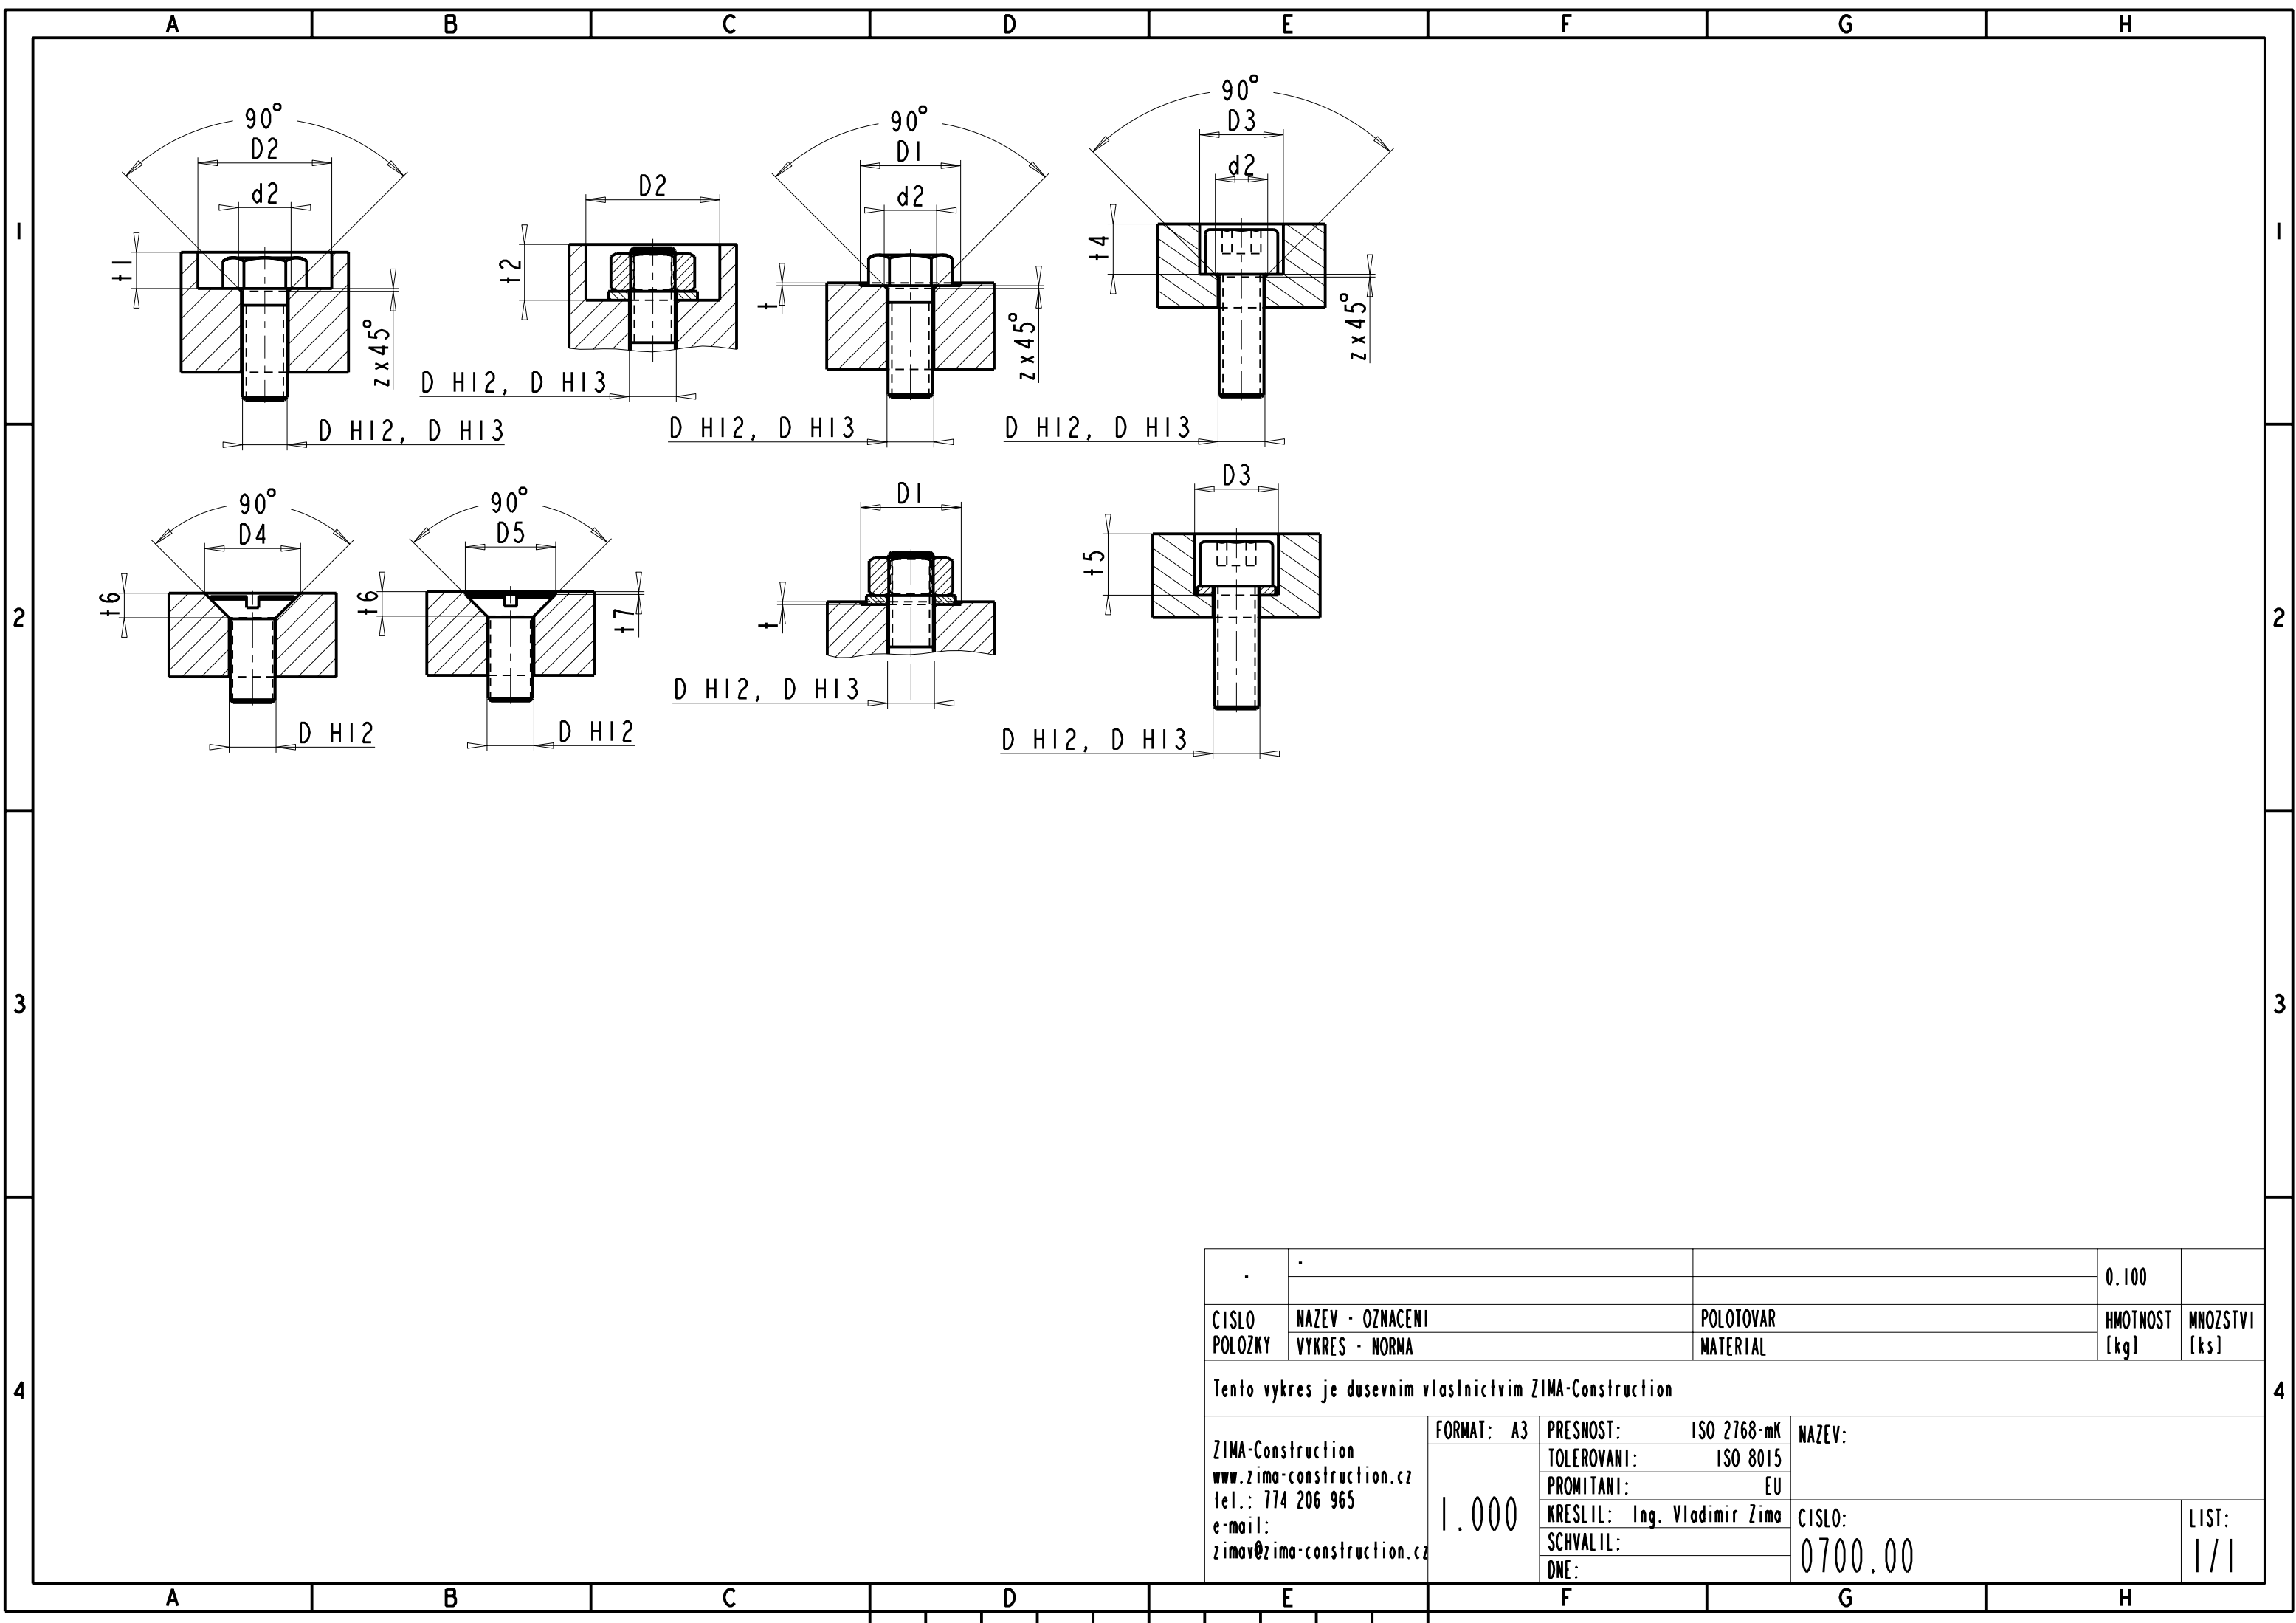

			0.100	
CÍSLO POLOŽKY	NAZEV - OZNACENÍ	POLOTOVAR	HMOTNOST [kg]	MNOŽSTVÍ [ks]
	VYKRES - NORMA	MATERIAL		
Tento výkres je duševním vlastnictvím ZIMA-Construction				
ZIMA-Construction www.zima-construction.cz tel.: 774 206 965 e-mail: zimav@zima-construction.cz		FORMAT: A3	PRESNOST: ISO 2768-mK	NAZEV:
		1.000	TOLEROVANI: ISO 8015	
			PROMITANI: EU	
			KRESLIL: Ing. Vladimír Zima	CÍSLO:
			SCHVALIL:	0700.00
		DNE:		LIST: 1/1